

Zyra kadastrale komunale / Opštinska katastarska kancelarija: Ferizaj

Zona kadastrale / Katastarska zona: Ferizaj

Lloji i njësisë kadastrale / Vrsta katastarske jedinice : Situacion objektit



Nr. i njësisë kadastrale / Br. katastarske jedinice : 03437-0


Numri i lëndës / Broj predmeta:

Shkalla e zvoglimit / Razmera plana : 1:250

Republika e Kosovës
Republika Kosova-Republic of Kosovo
Qeveria -Vlada-Government

Ministria e Mjedisit dhe Planifikimit Hapësinor /Ministarstvo Sredine i Prostornog Planiranja/Ministry of Environment and Spatial Planning
AGJENCIA KADASTRALE E KOSOVËS/ KATASTARSKA AGENCIJA KOSOVA/ KOSOVA CADASTRAL AGENCY

Pronar: " Macropus Group SH.P.K. " Numri biznesit: 810145038

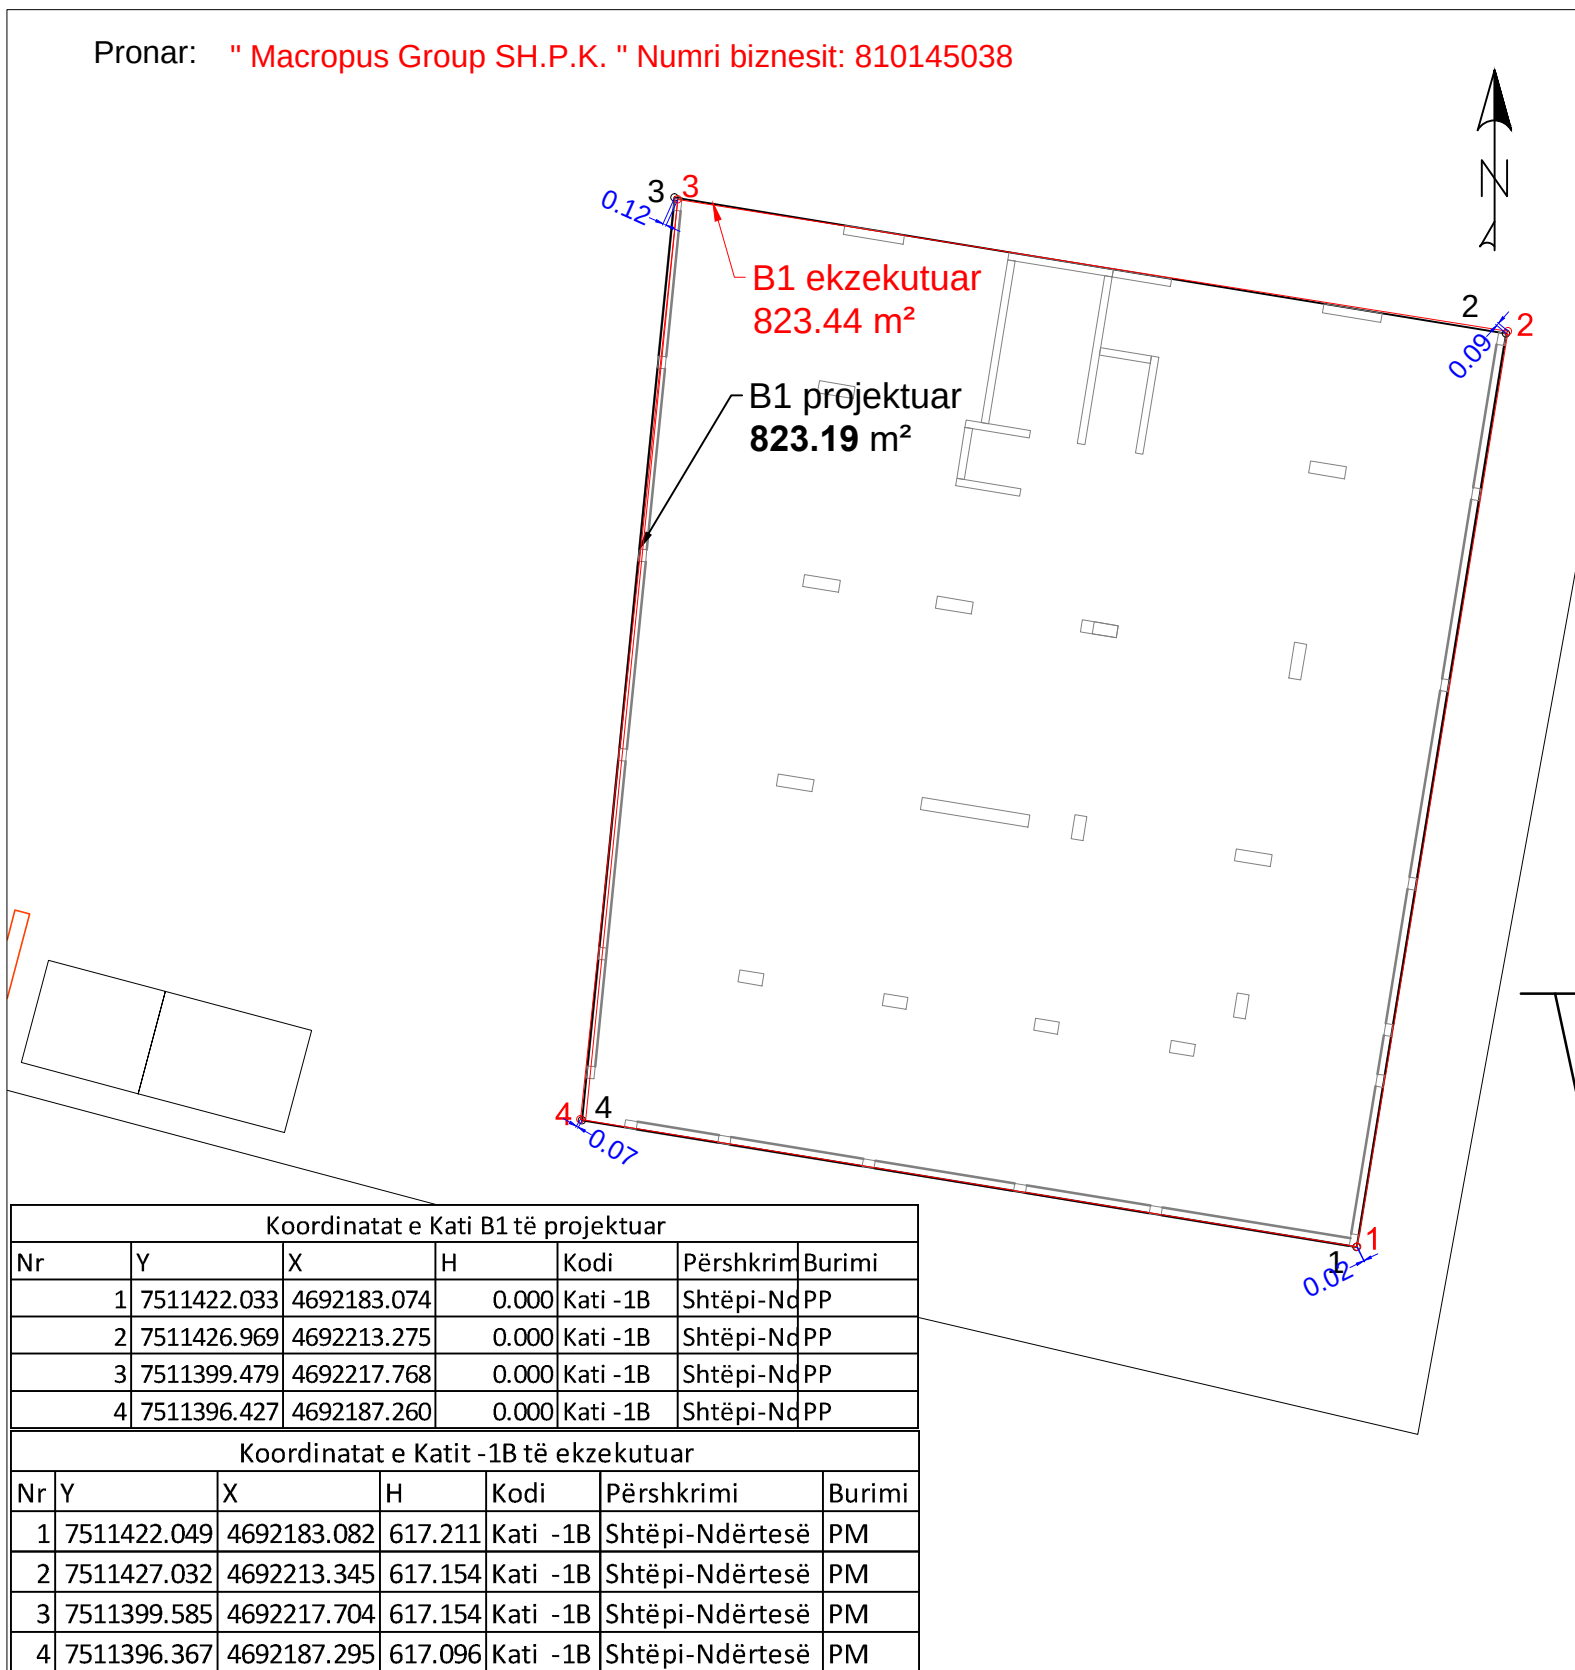

Rilevoi / Snimio: Liridon Sejdiu
(emri dhe mbiemri i gjeodetit/kompanisë/ ime i prezime geodeta/ kompanije)

Etazha: Kati -1B

Nr. i licencës / Br. licence: 140

V.V.

Nënshkrimi / Potpis:

Data e rilevimit / Datum snimanja: 03/11/2025

Data e aprovimit / Datum usvajanja: