

Zyra kadastrale komunale / Opštinska katastarska kancelarija: Ferizaj

Zona kadastrale / Katastarska zona: Ferizaj

Lloji i njësisë kadastrale / Vrsta katastarske jedinice : Situacion objektit



Nr. i njësisë kadastrale / Br. katastarske jedinice : 03437-0


Numri i lëndës / Broj predmeta:

Shkalla e zvoglimit / Razmera plana : 1:250

Republika e Kosovës
Republika Kosova-Republic of Kosovo
Qeveria -Vlada-Government

Ministria e Mjedisit dhe Planifikimit Hapësinor /Ministarstvo Sredine i Prostornog Planiranja/Ministry of Environment and Spatial Planning
AGJENCIA KADASTRALE E KOSOVËS/ KATASTARSKA AGENCIJA KOSOVA/ KOSOVA CADASTRAL AGENCY

Pronar: " Macropus Group SH.P.K. " Numri biznesit: 810145038

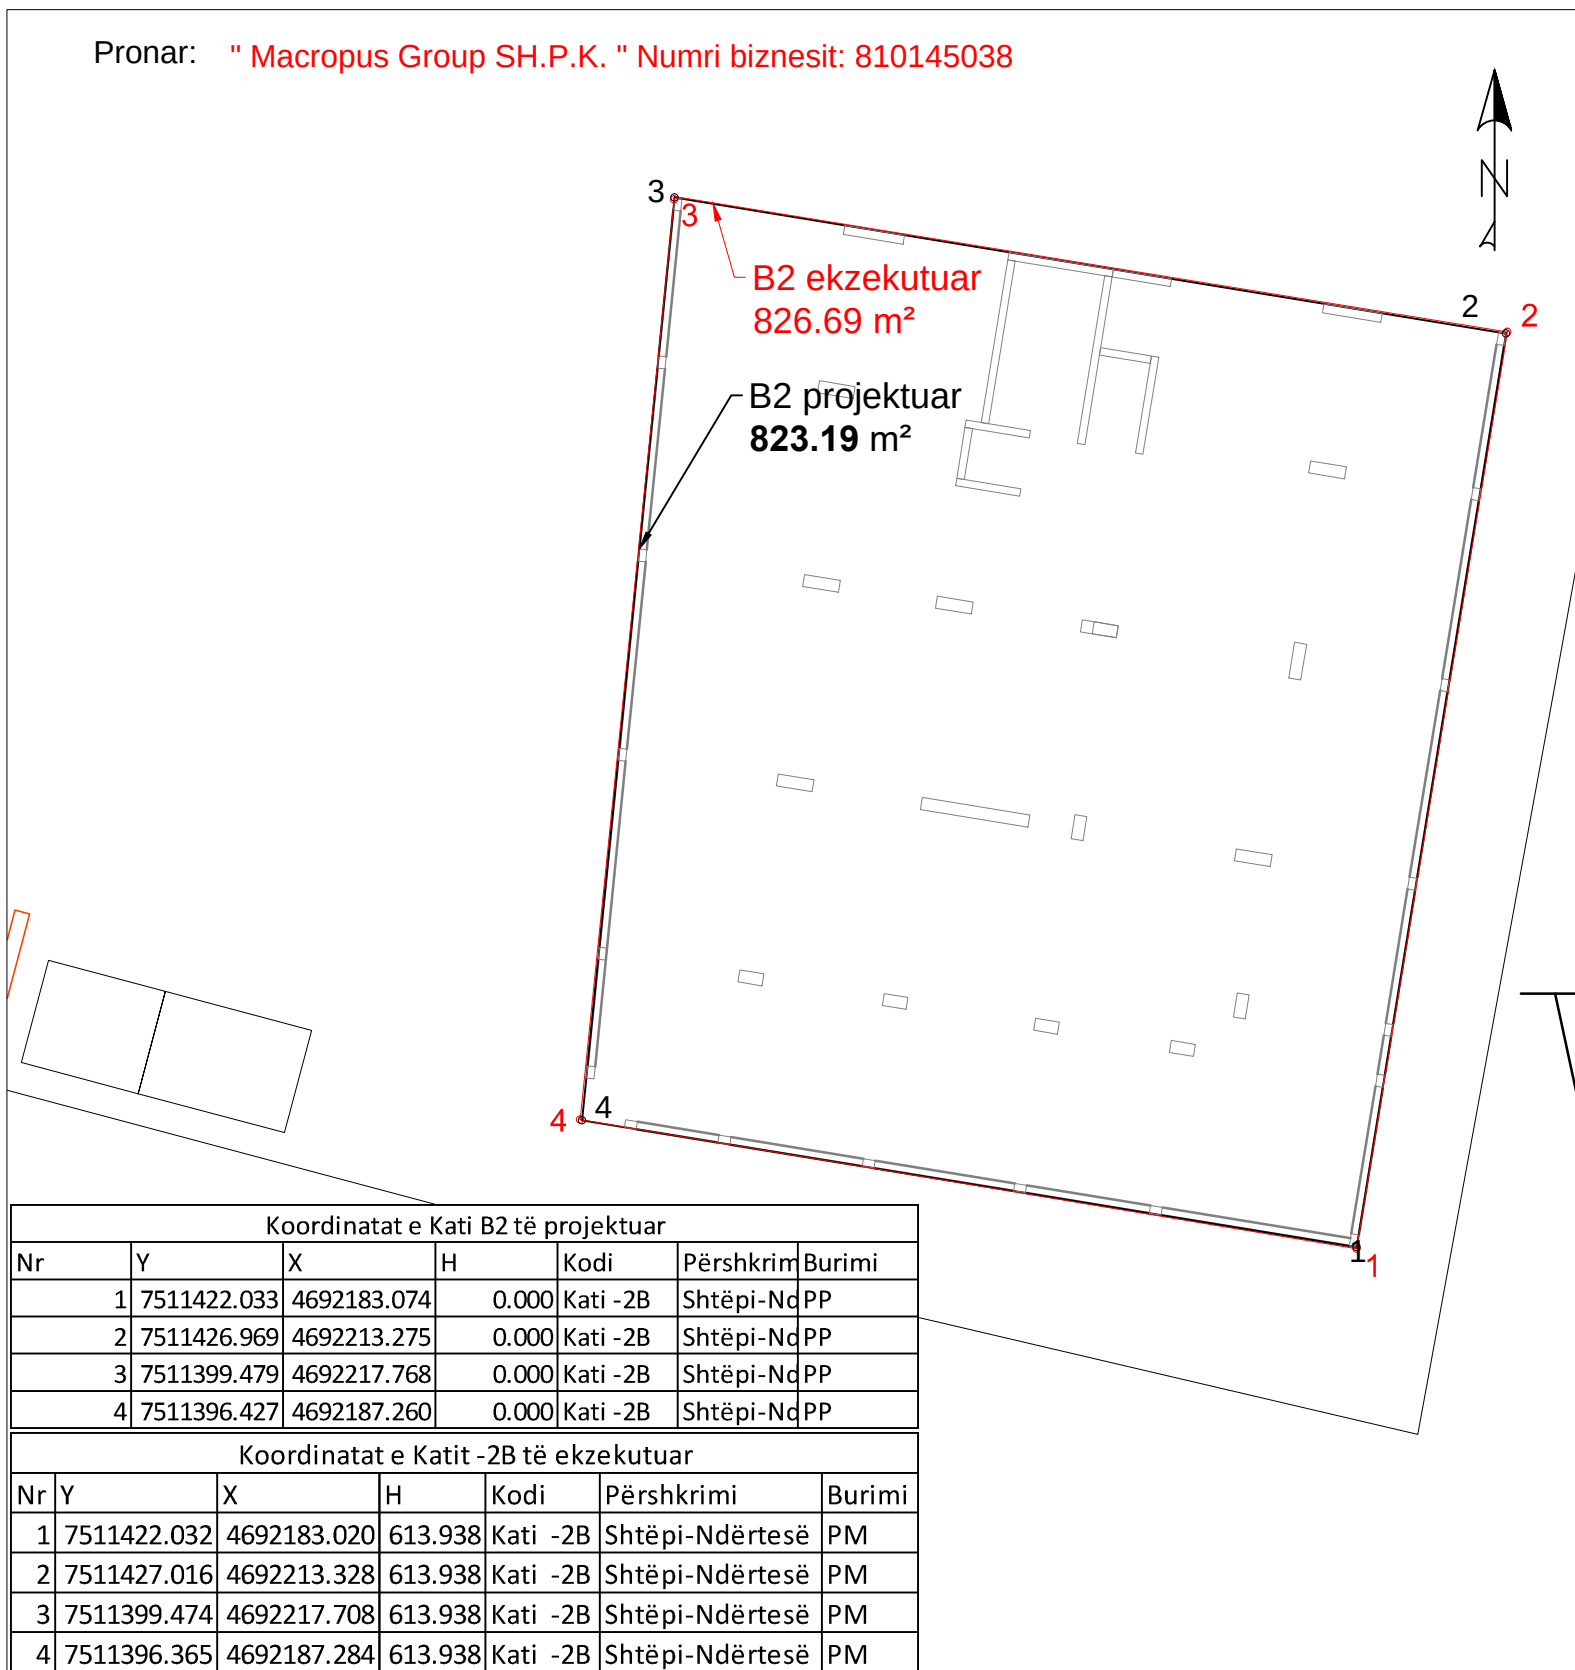

Koordinatat e Kati B2 të projektuar

Nr	Y	X	H	Kodi	Përshkrim	Burimi
1	7511422.033	4692183.074	0.000	Kati -2B	Shtëpi-Nd PP	
2	7511426.969	4692213.275	0.000	Kati -2B	Shtëpi-Nd PP	
3	7511399.479	4692217.768	0.000	Kati -2B	Shtëpi-Nd PP	
4	7511396.427	4692187.260	0.000	Kati -2B	Shtëpi-Nd PP	

Koordinatat e Katit -2B të ekzekutuar

Nr	Y	X	H	Kodi	Përshkrimi	Burimi
1	7511422.032	4692183.020	613.938	Kati -2B	Shtëpi-Ndërtesë	PM
2	7511427.016	4692213.328	613.938	Kati -2B	Shtëpi-Ndërtesë	PM
3	7511399.474	4692217.708	613.938	Kati -2B	Shtëpi-Ndërtesë	PM
4	7511396.365	4692187.284	613.938	Kati -2B	Shtëpi-Ndërtesë	PM

Rilevoi / Snimio: Liridon Sejdiu
(emri dhe mbiemri i gjeodetit/kompanisë/ ime i prezime geodeta/ kompanije)

Etazha: Kati -2B

Nr. i licencës / Br. licence: 140

V.V.

Nënshkrimi / Potpis:

Nënshkrimi / Potpis:

Data e rilevimit / Datum snimanja: 23/09/2025

Data e aprovimit / Datum usvajanja: